


495 Central Ave
Northfield, IL 60093


INTERIORS

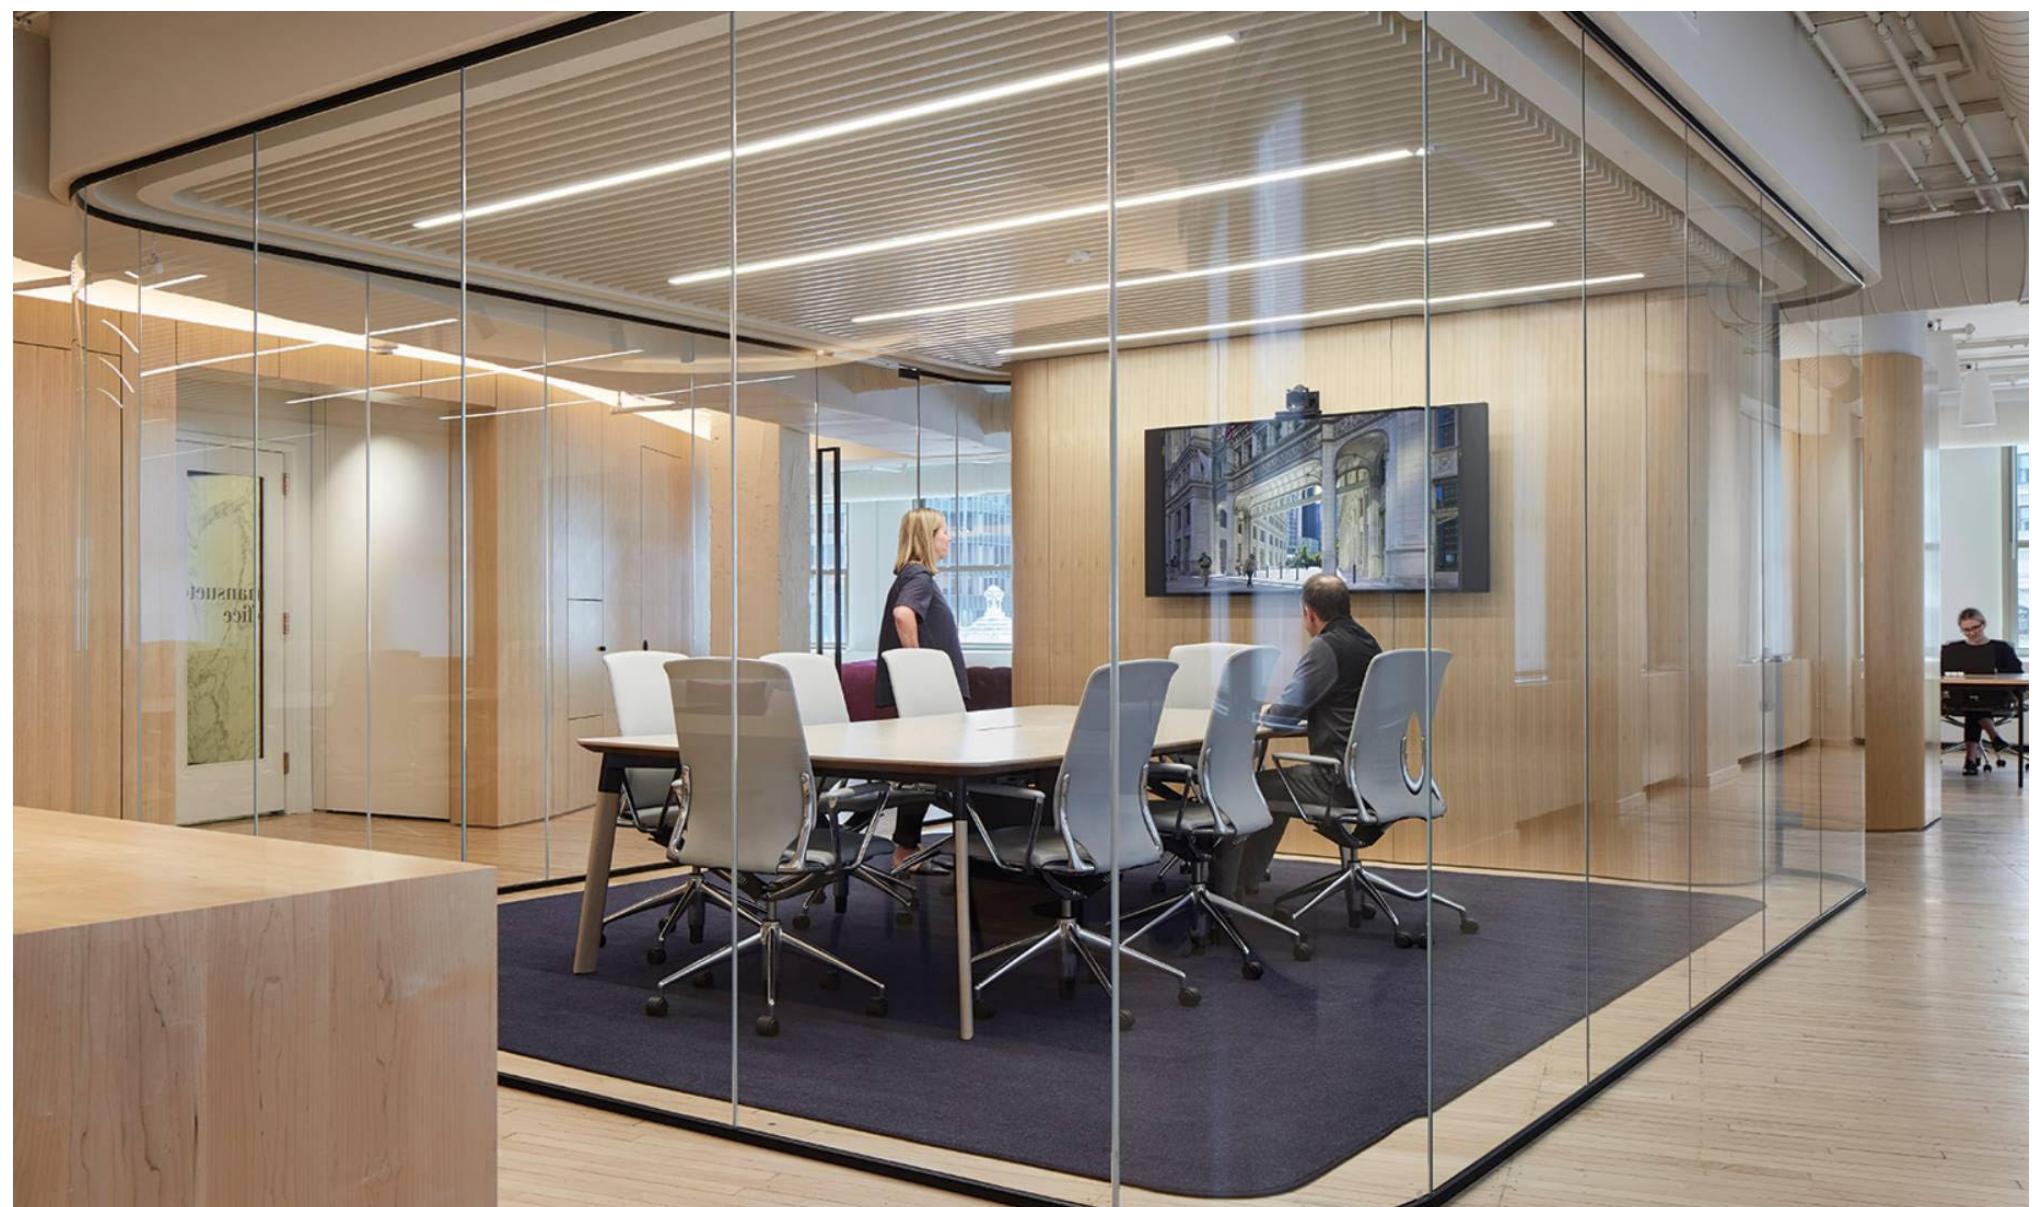


1 GLASS-ENCLOSED CONFERENCE ROOM



4 ZEN DEN / MULTI-PURPOSE ROOM

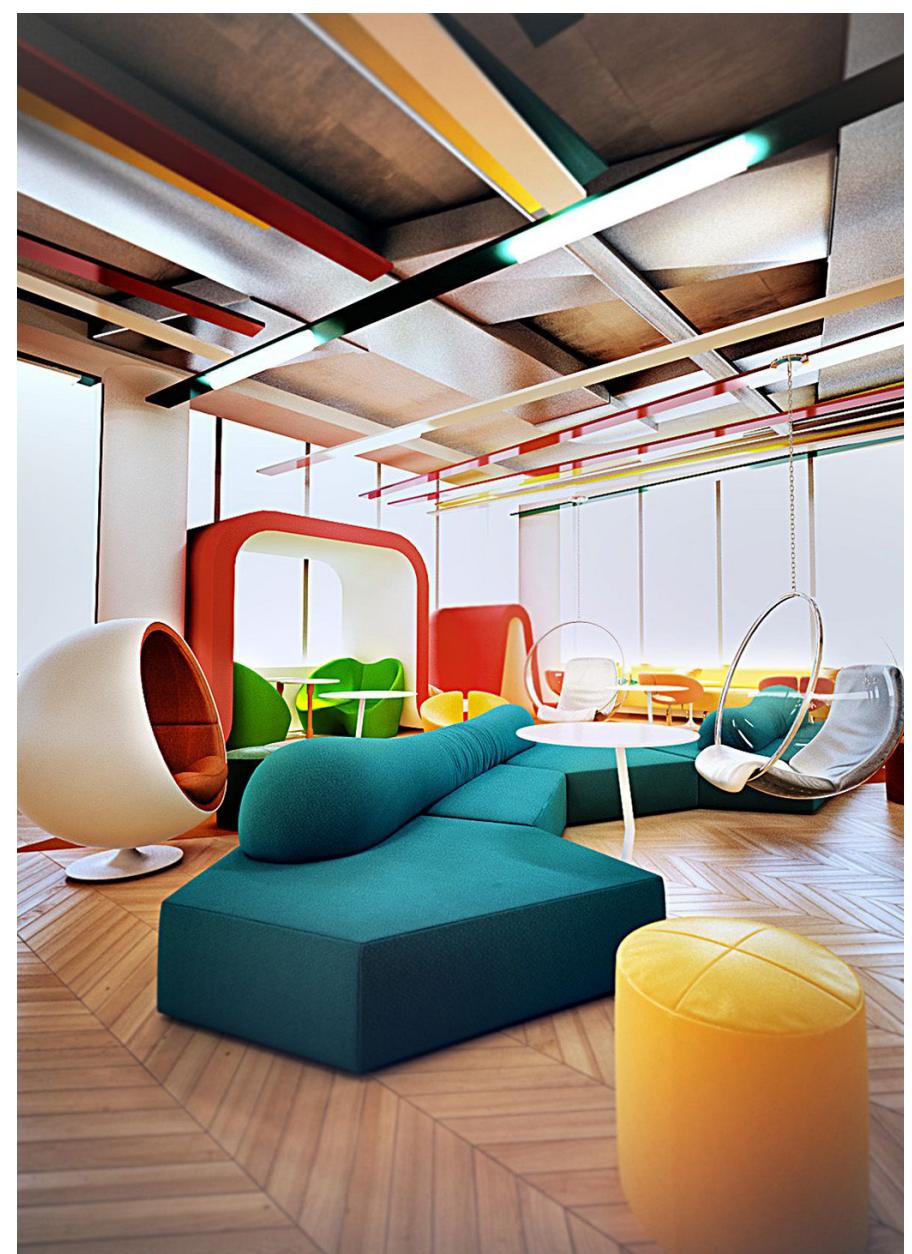


4 ZEN DEN / MULTI-PURPOSE ROOM

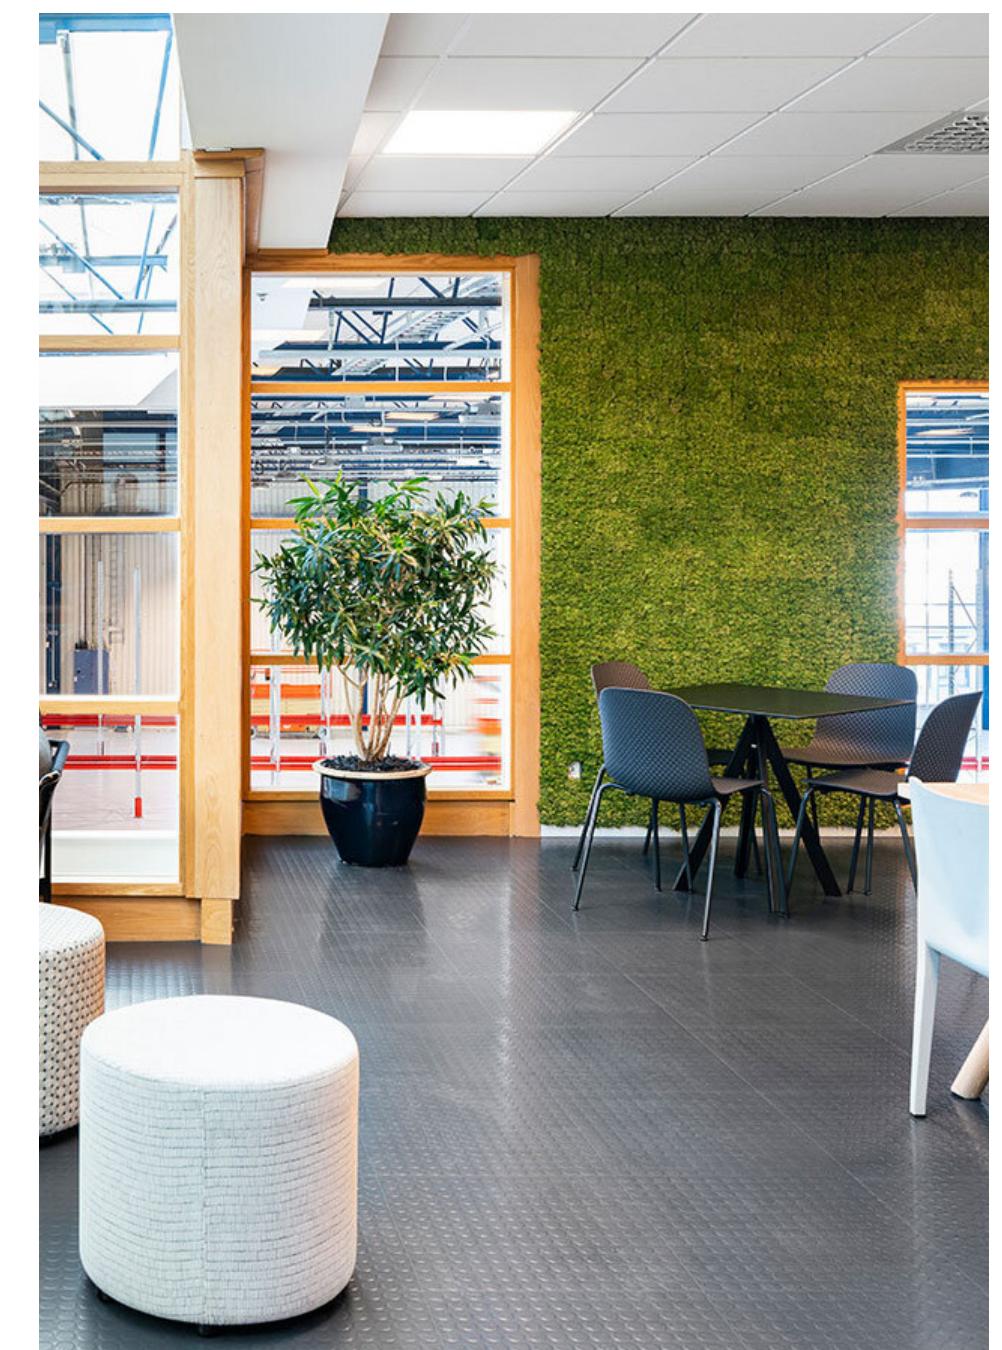


5 MOSS WALL




5 MOSS WALL: FREESTANDING

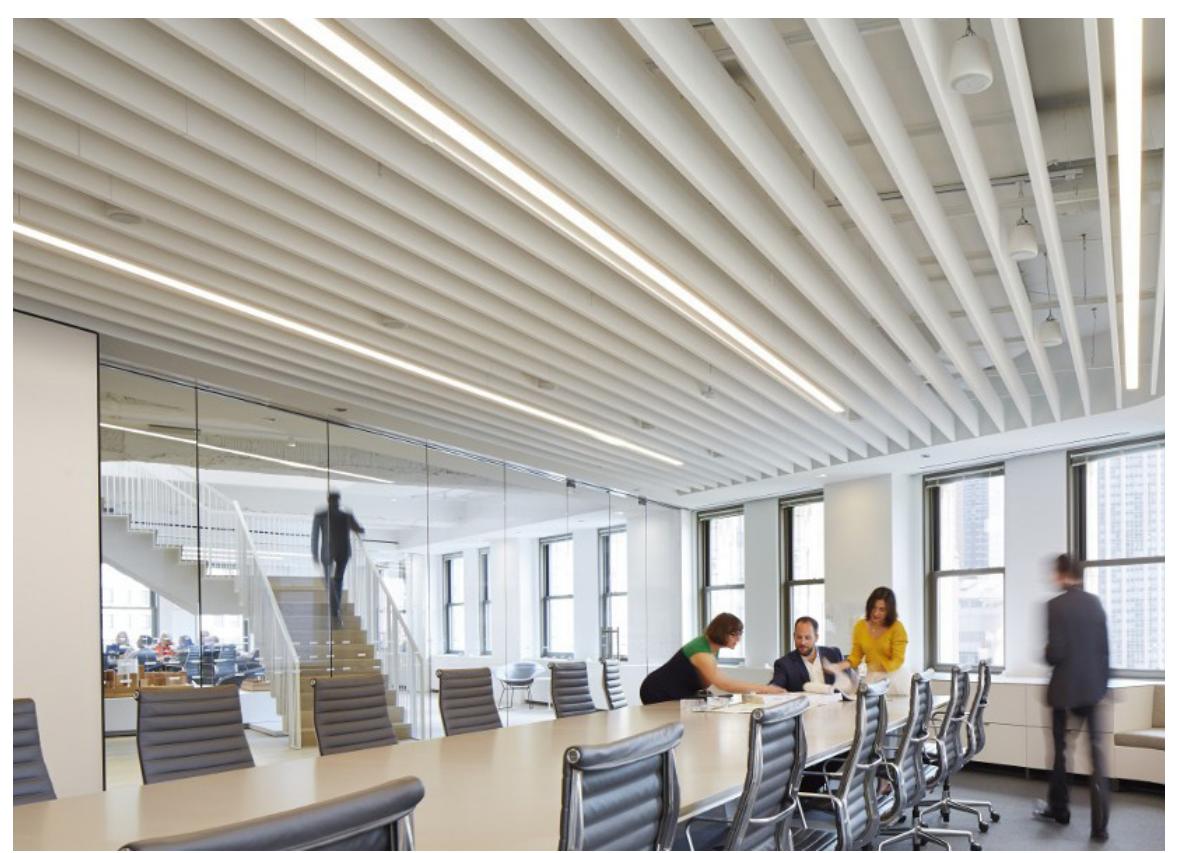


2 CEILING: BAFFLES

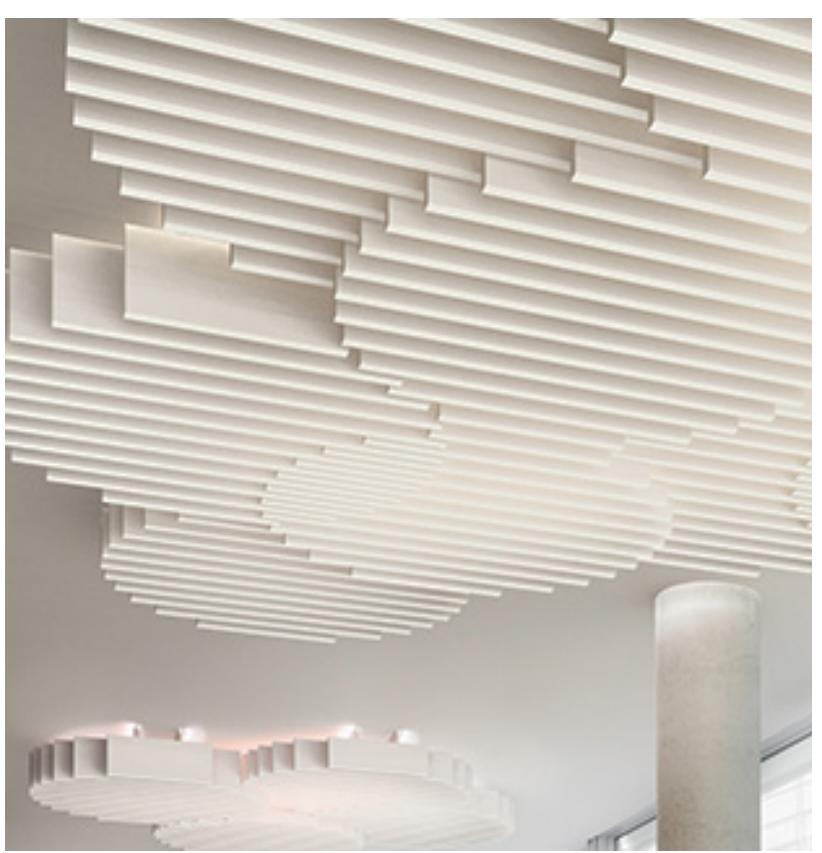


2 CEILING: BAFFLES

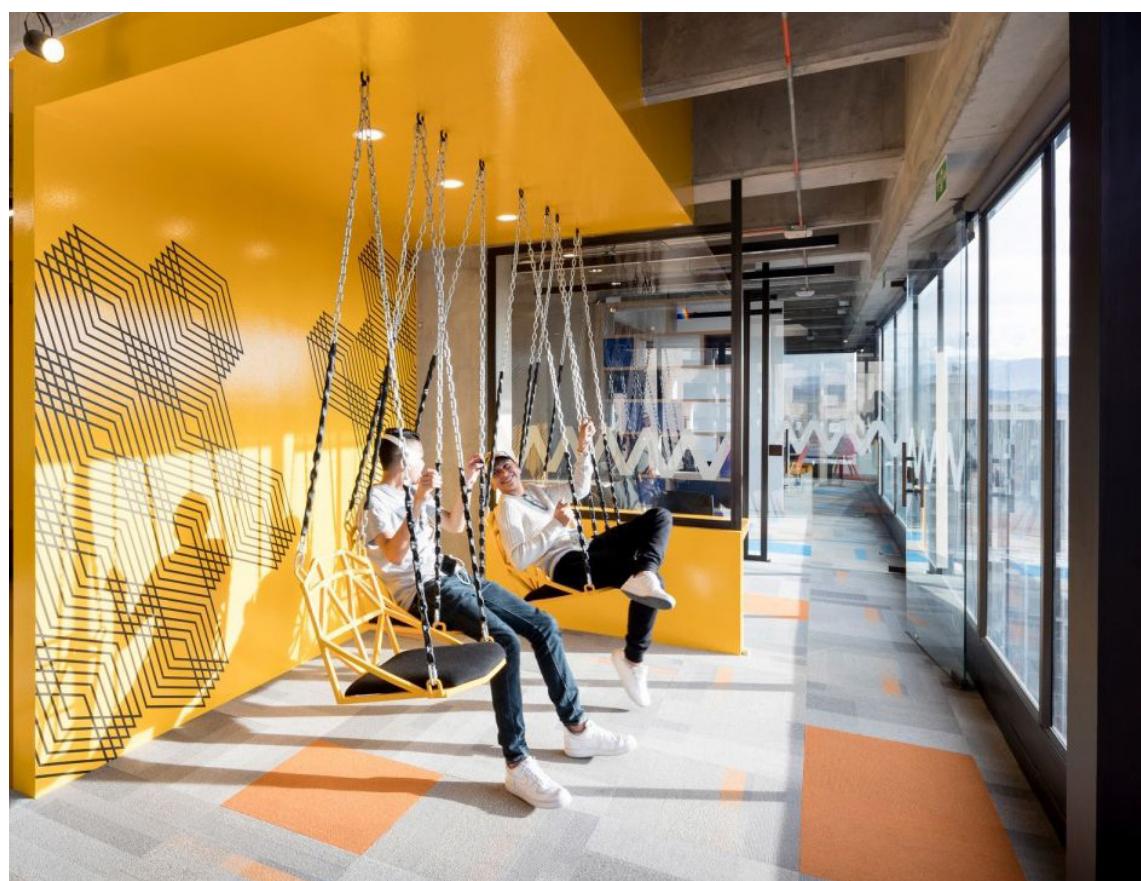

4 ZEN DEN / MULTI-PURPOSE ROOM

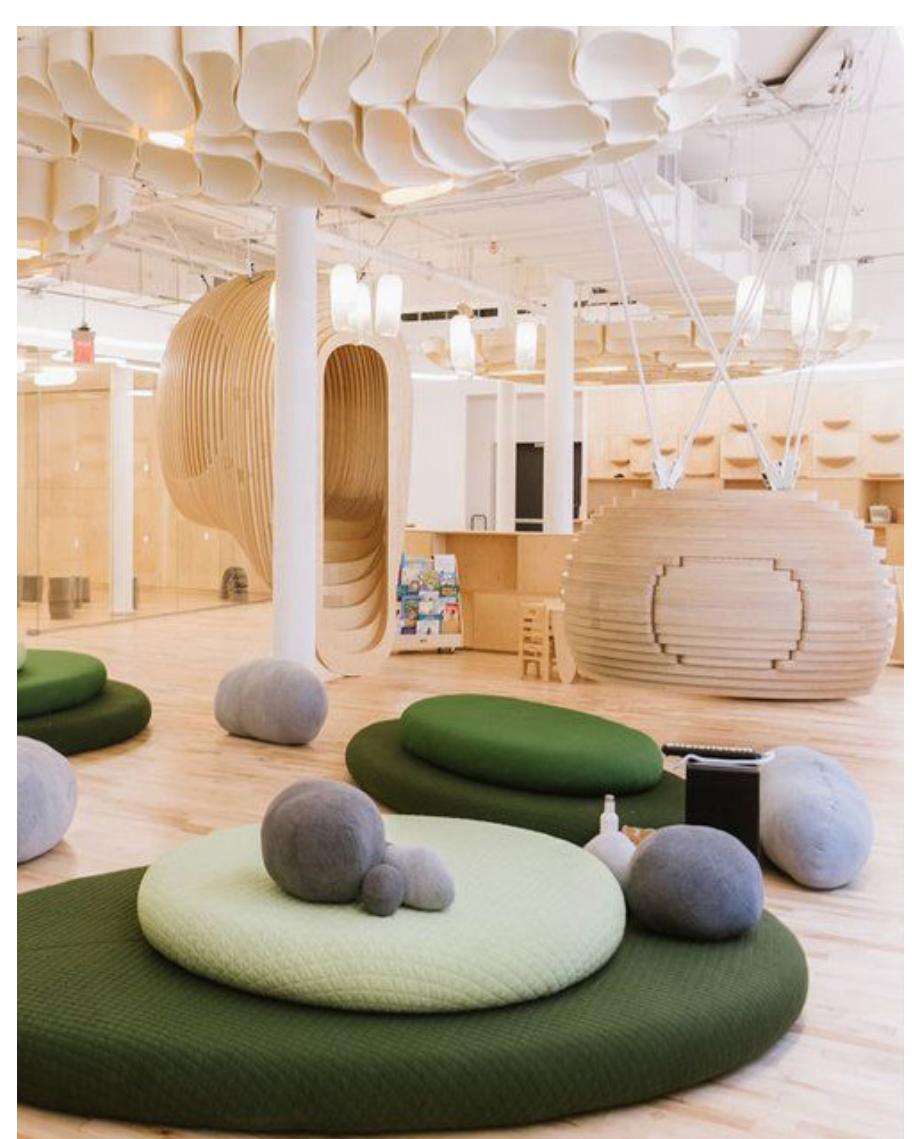

4 ZEN DEN / MULTI-PURPOSE ROOM

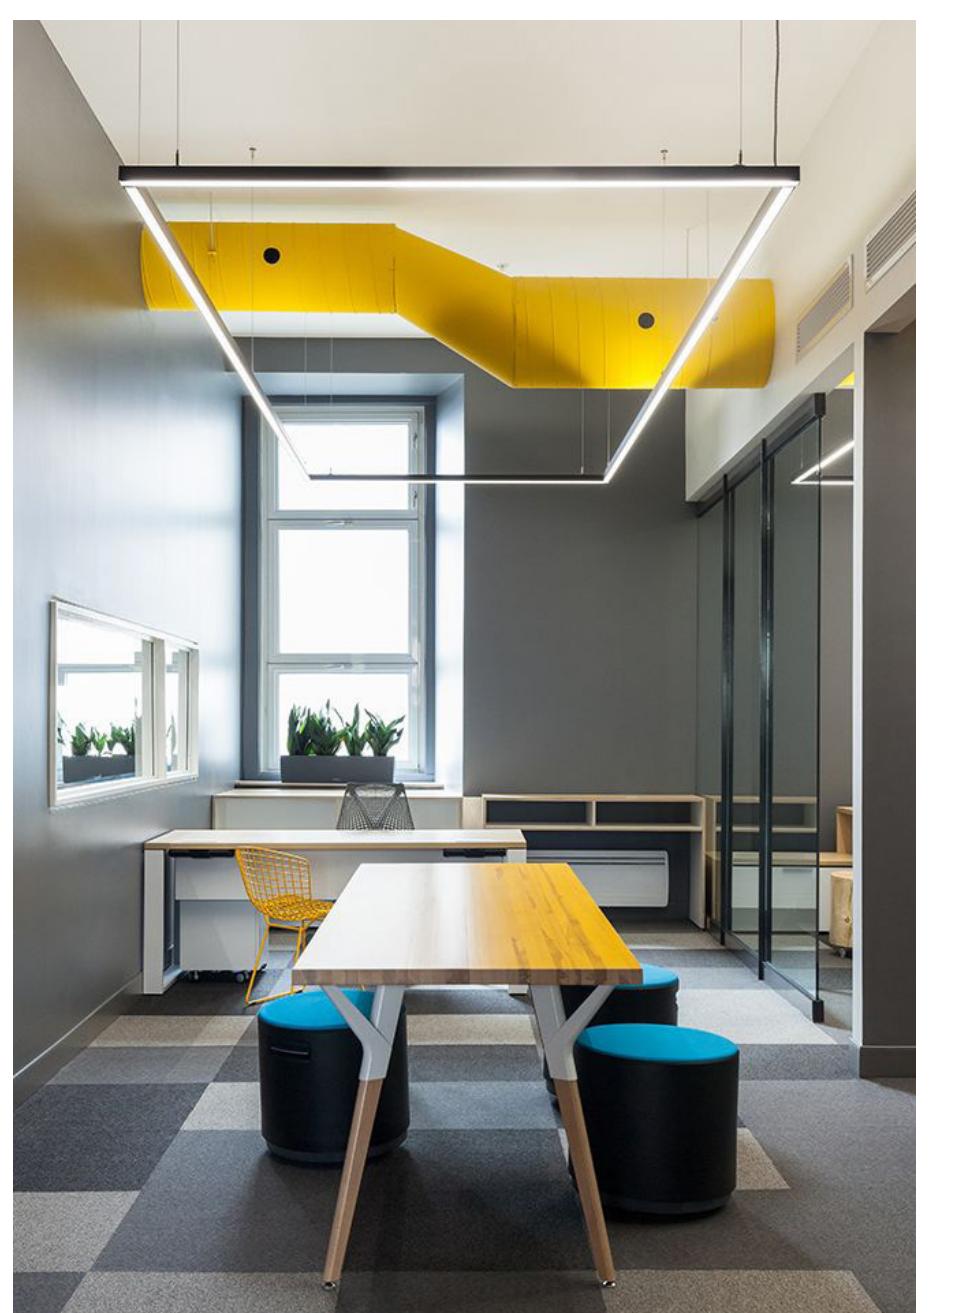

2 CEILING: LINEAR LED LIGHTING




3 WATER FEATURE / WATER WALL




4 RELAXATION NOOK




4 ZEN DEN / MULTI-PURPOSE ROOM

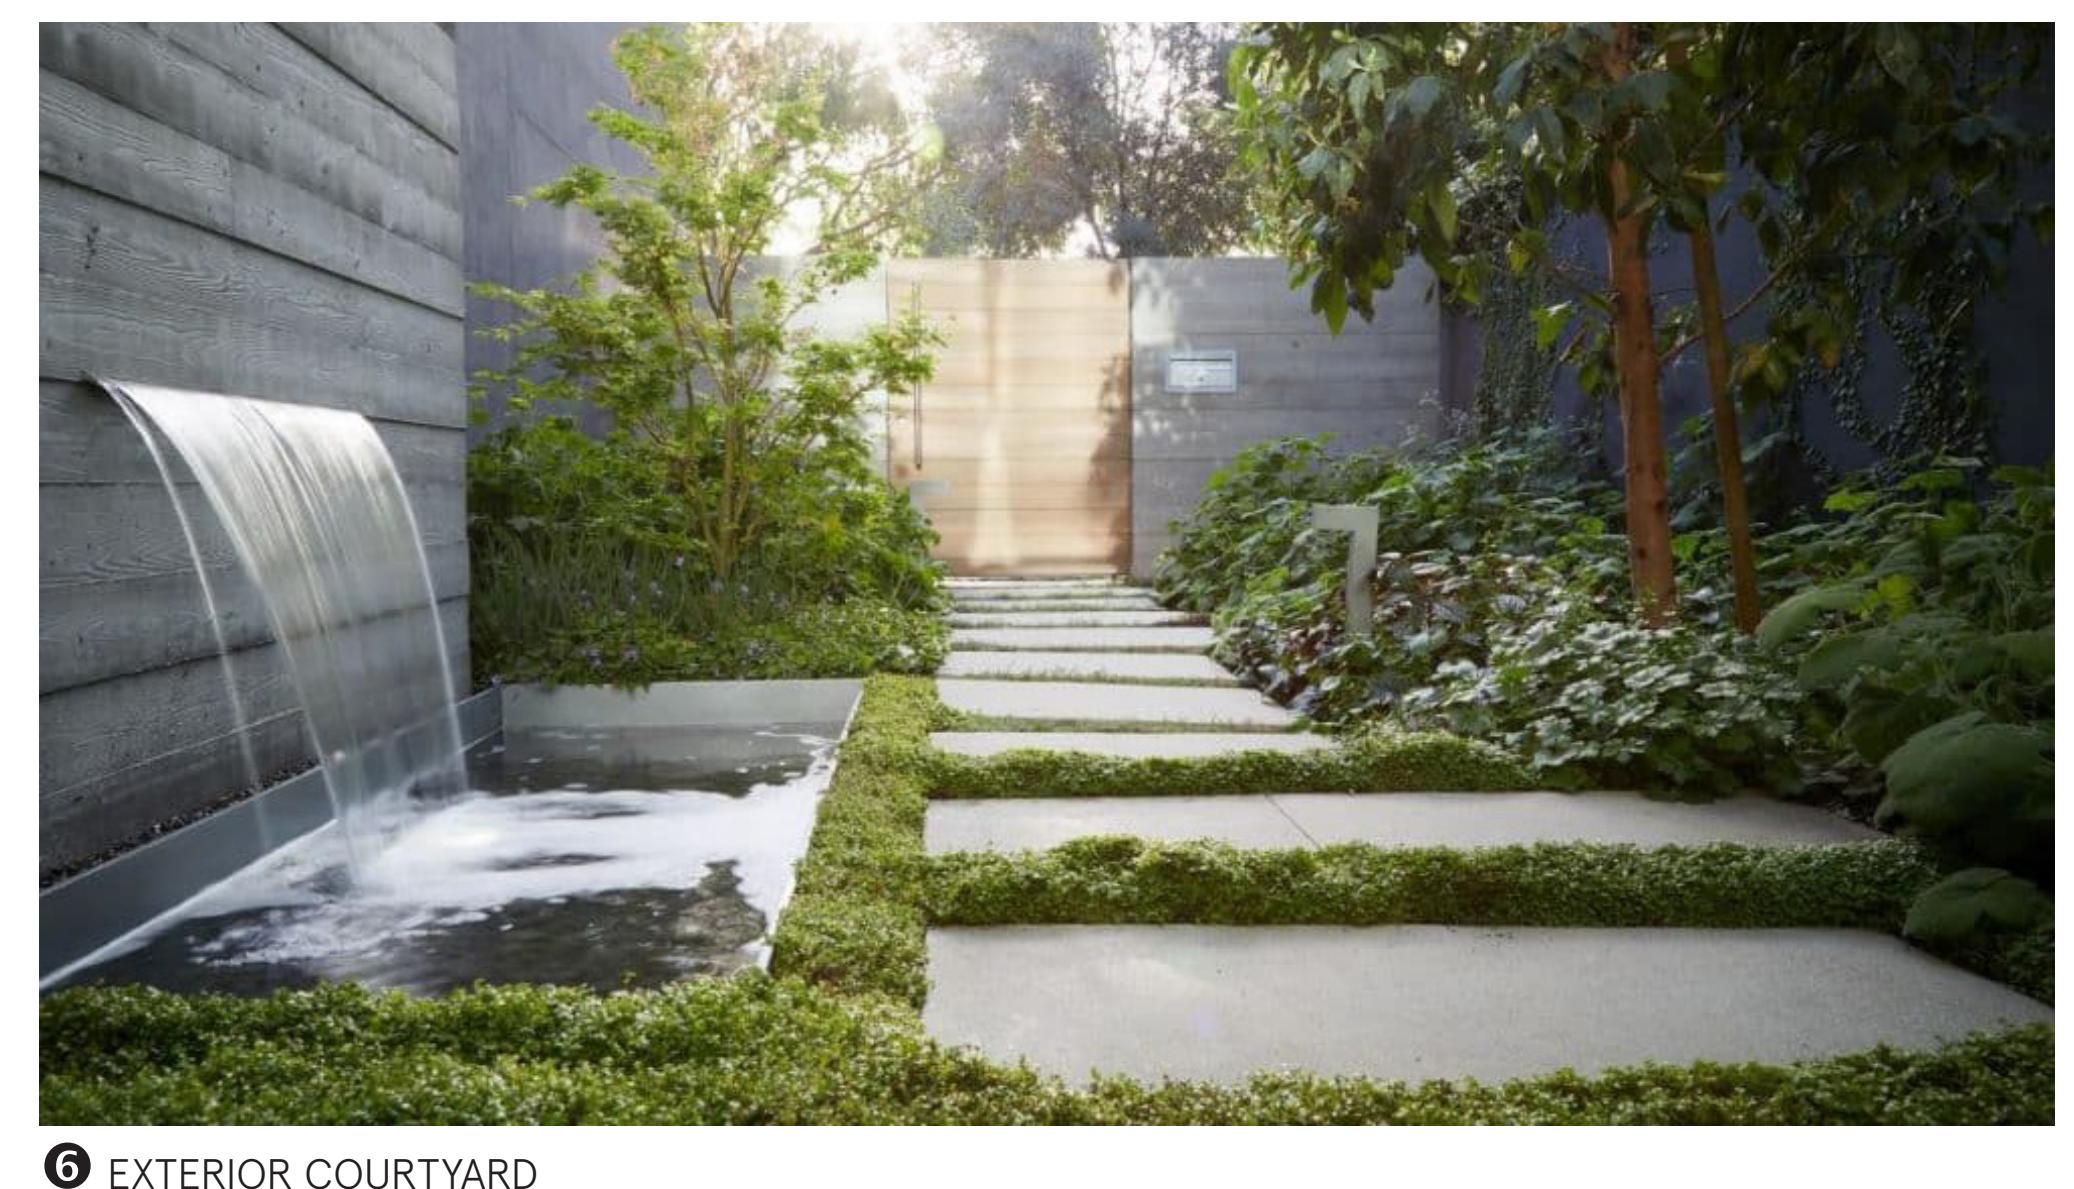

6 EXTERIOR COURTYARD

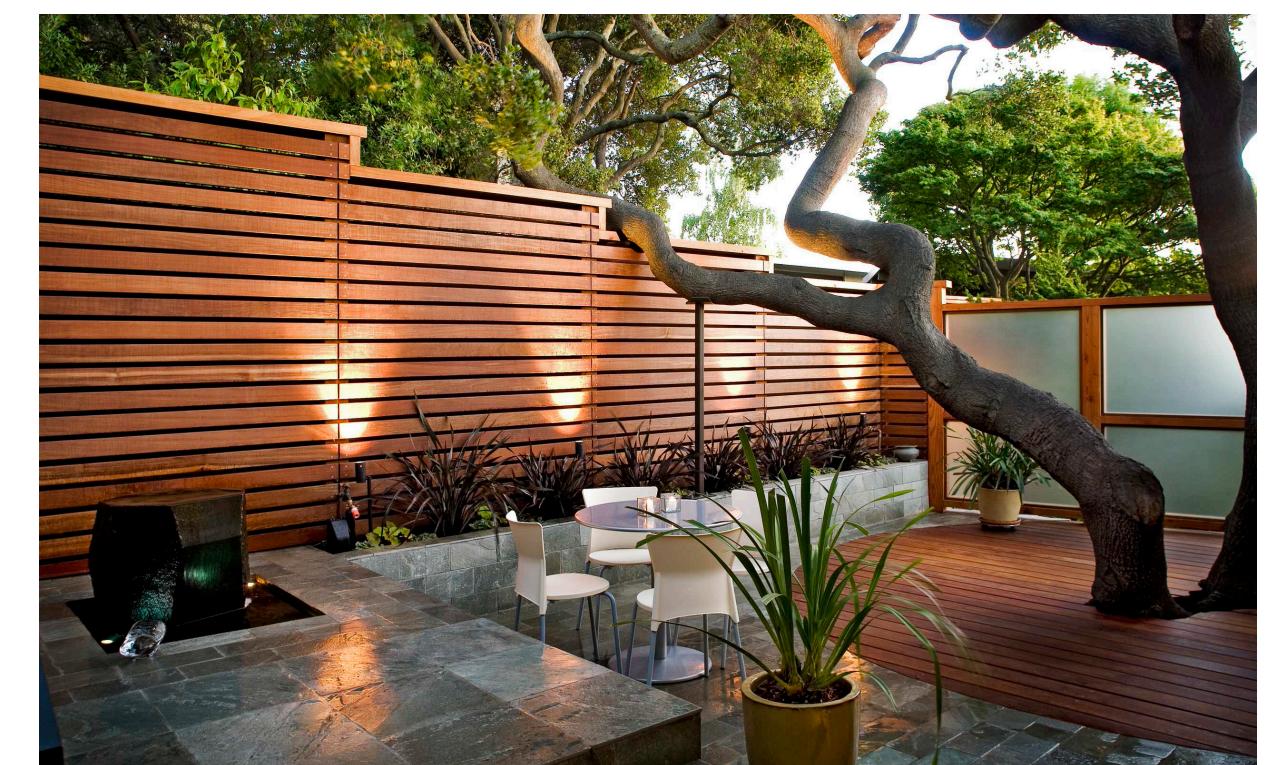

6 EXTERIOR COURTYARD

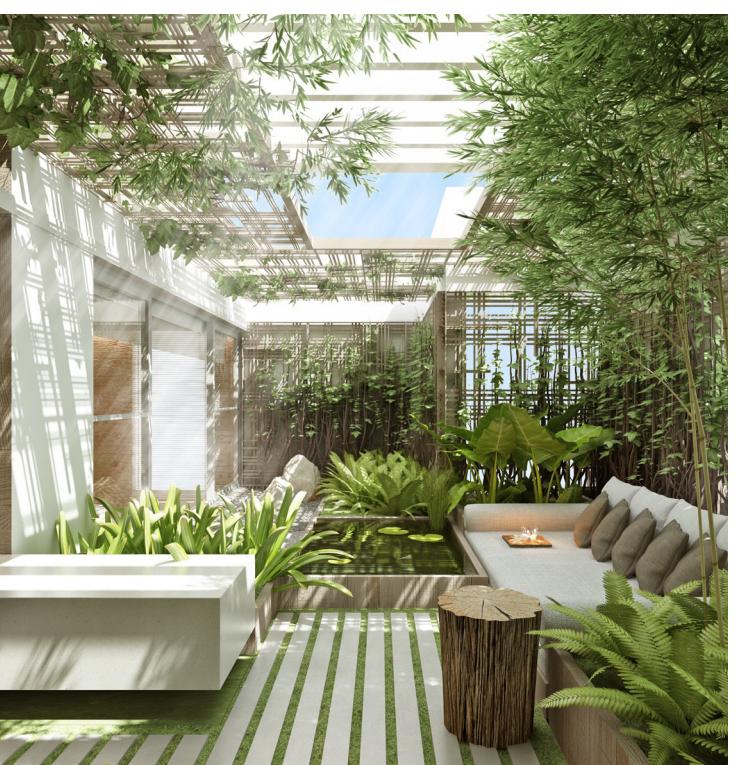

6 EXTERIOR COURTYARD

495 Central Ave
Northfield, IL 60093


GROUND FLOOR PLAN



JUNE 7, 2021 | SCALE: 1/4" = 1'-0"

495 Central Ave
Northfield, IL 60093

SECOND FLOOR PLAN

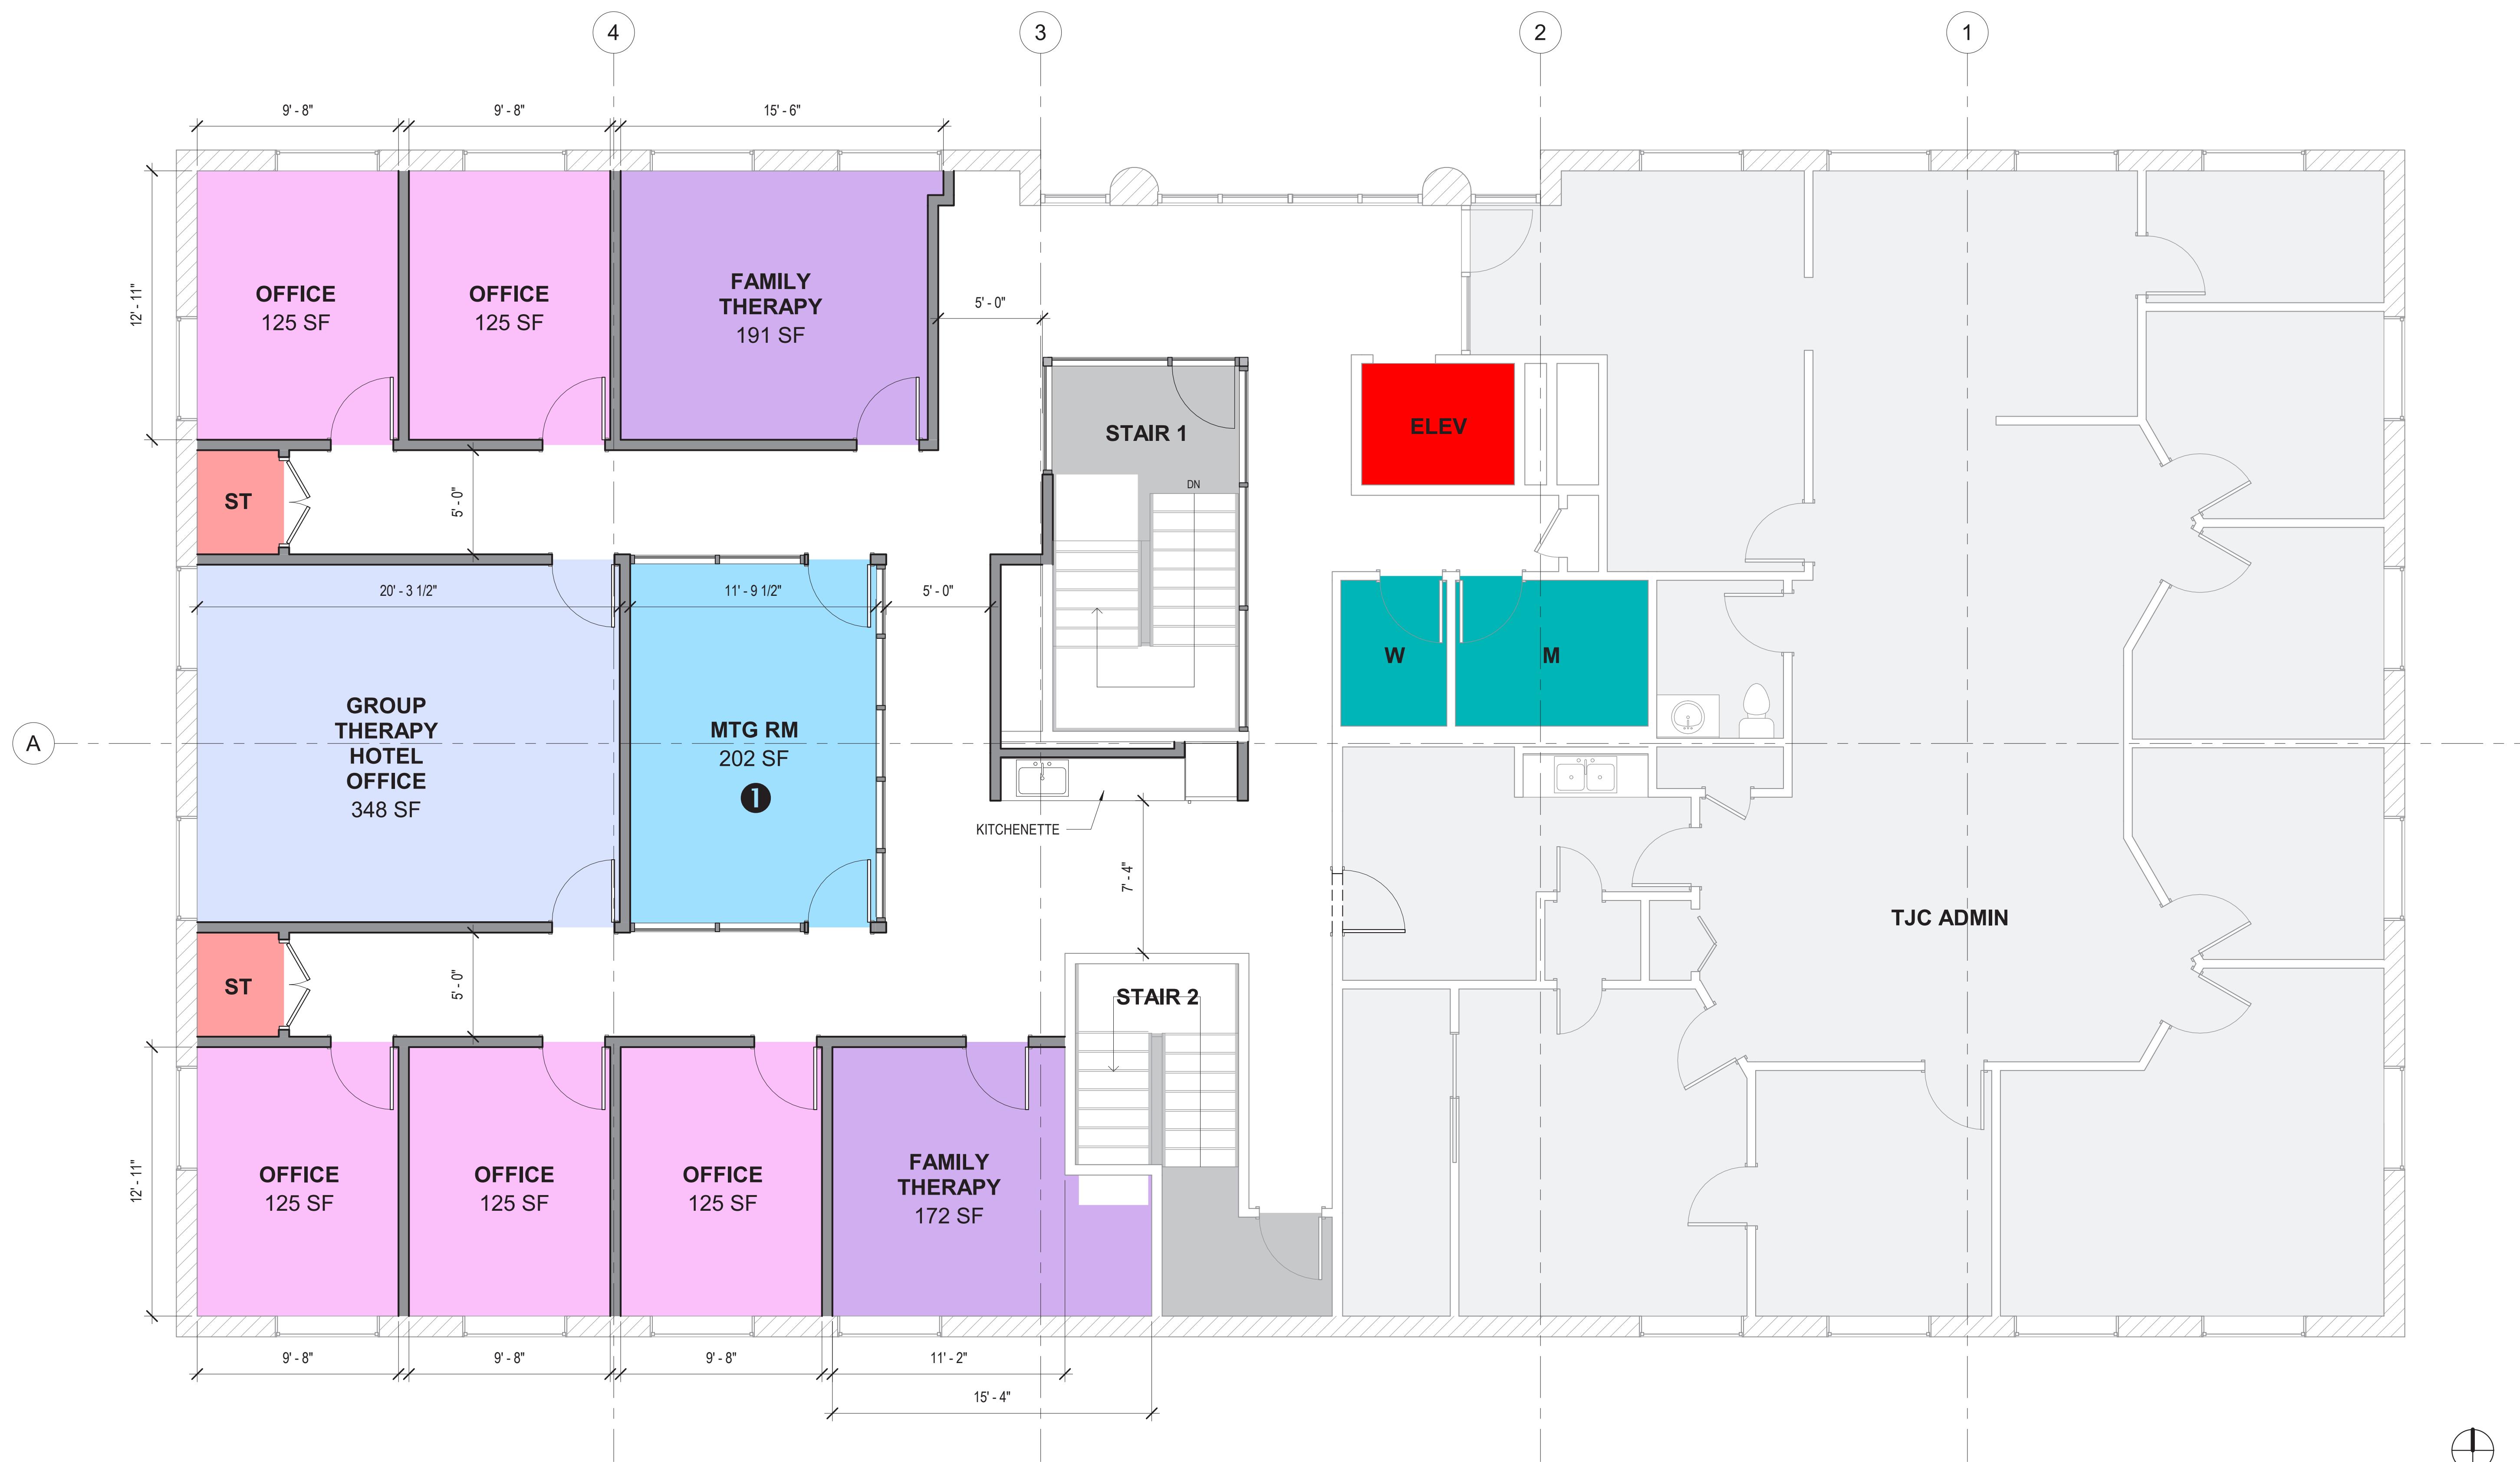

JUNE 7, 2021 | SCALE: 1/4" = 1'-0"